

POSITIONNEMENT DES ÉQUIPEMENTS


(VUE LATÉRALE DROIT)

STORE FIAMMA
3,2M

BAIE COULISSANTE
APSYS 1000X500

AÉRATION BASSE
186*480

PRISE P17

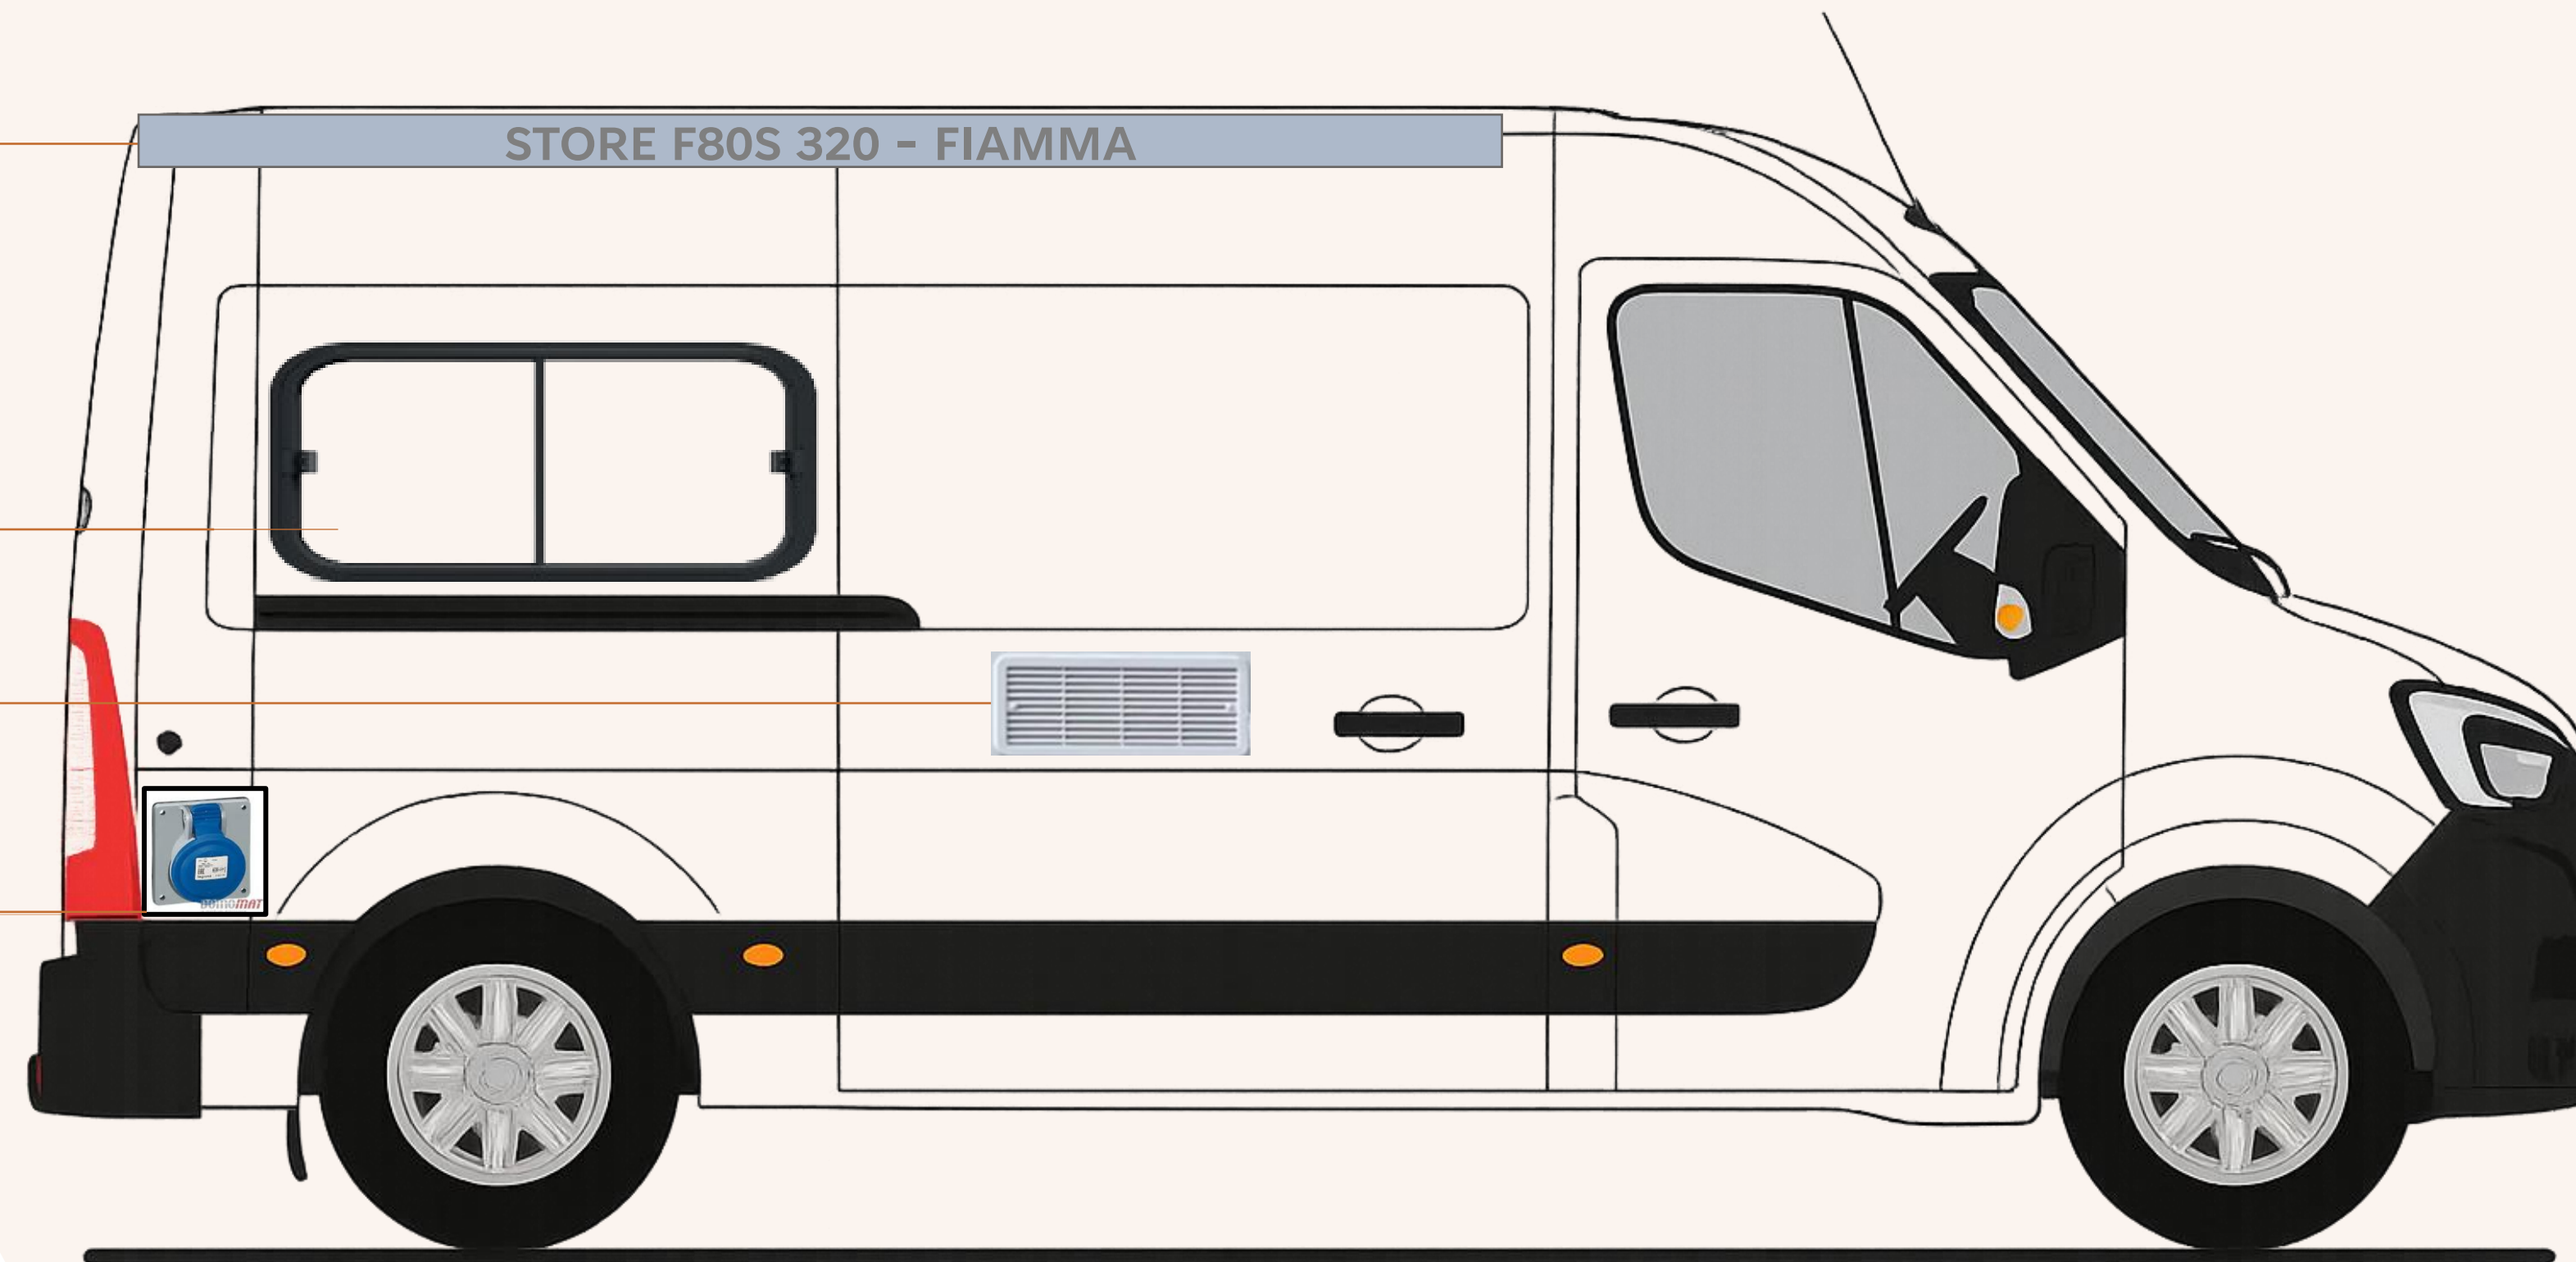

POSITIONNEMENT DES ÉQUIPEMENTS

(VUE LATÉRALE GAUCHE)


LANTERNEAU
THULE OMNIVENT
40X40

2X PANNEAU
SOLAIRE 200W

BAIE COULISSANTE
APSYS 1000X500

COUPELLE DE
REEMPLISSAGE
D'EAU

JET D'EAU
EXTÉRIEUR

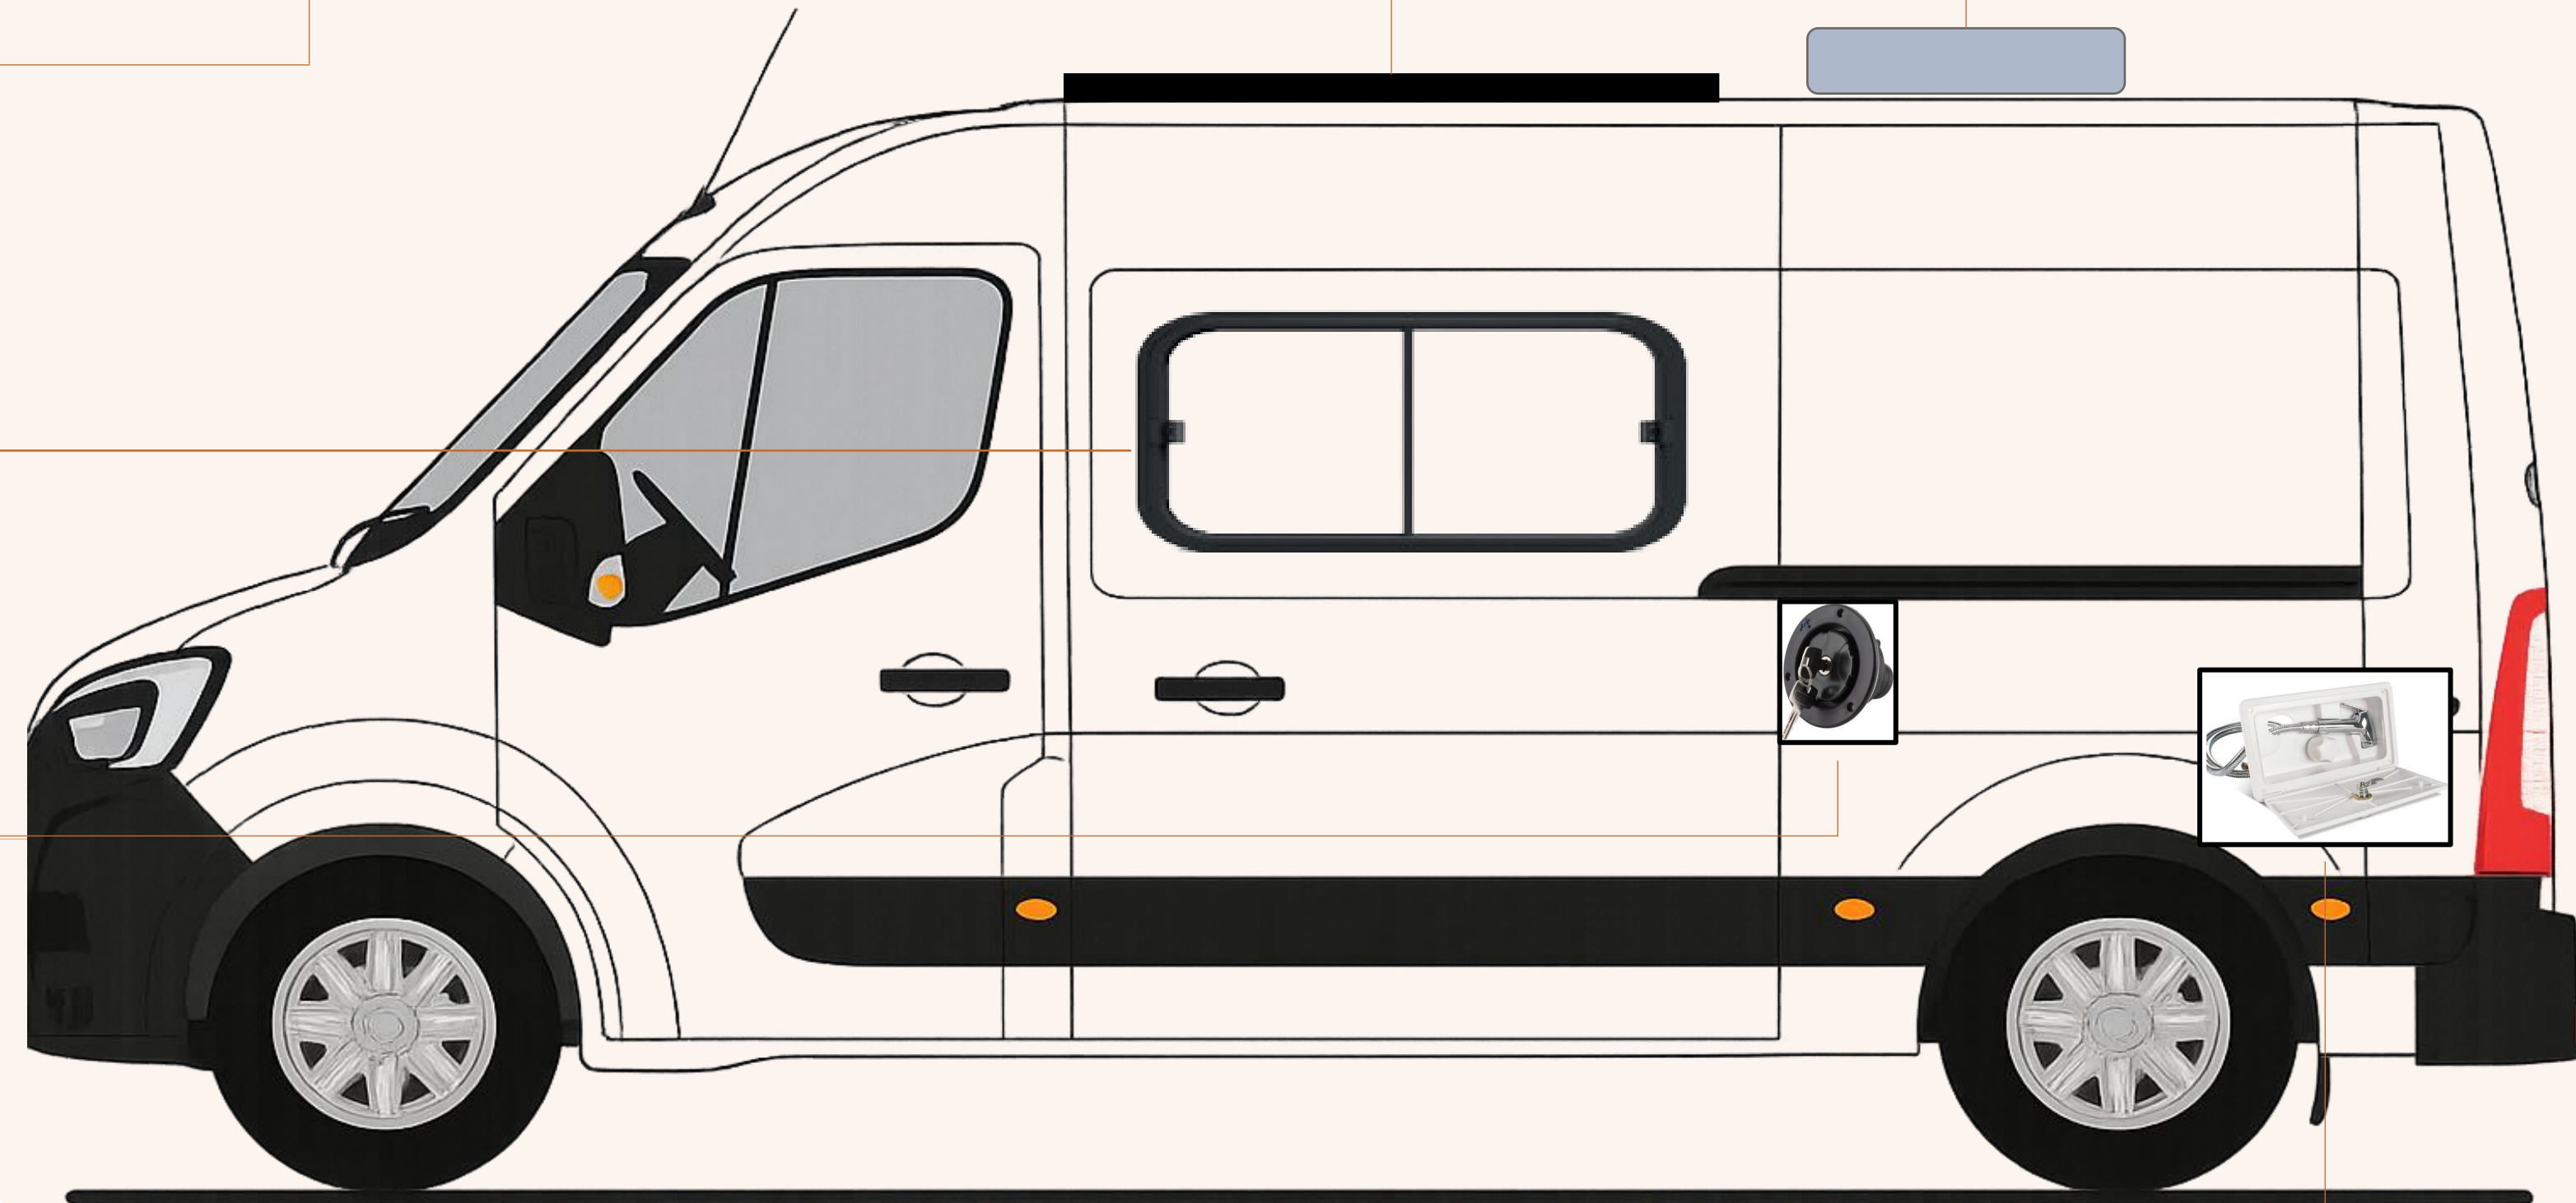


POSITIONNEMENT DES ÉQUIPEMENTS

(VUE SUPÉRIEURE)

LANTERNEAU
THULE OMNIVENT
40X40

2X PANNEAU SOLAIRE
200W

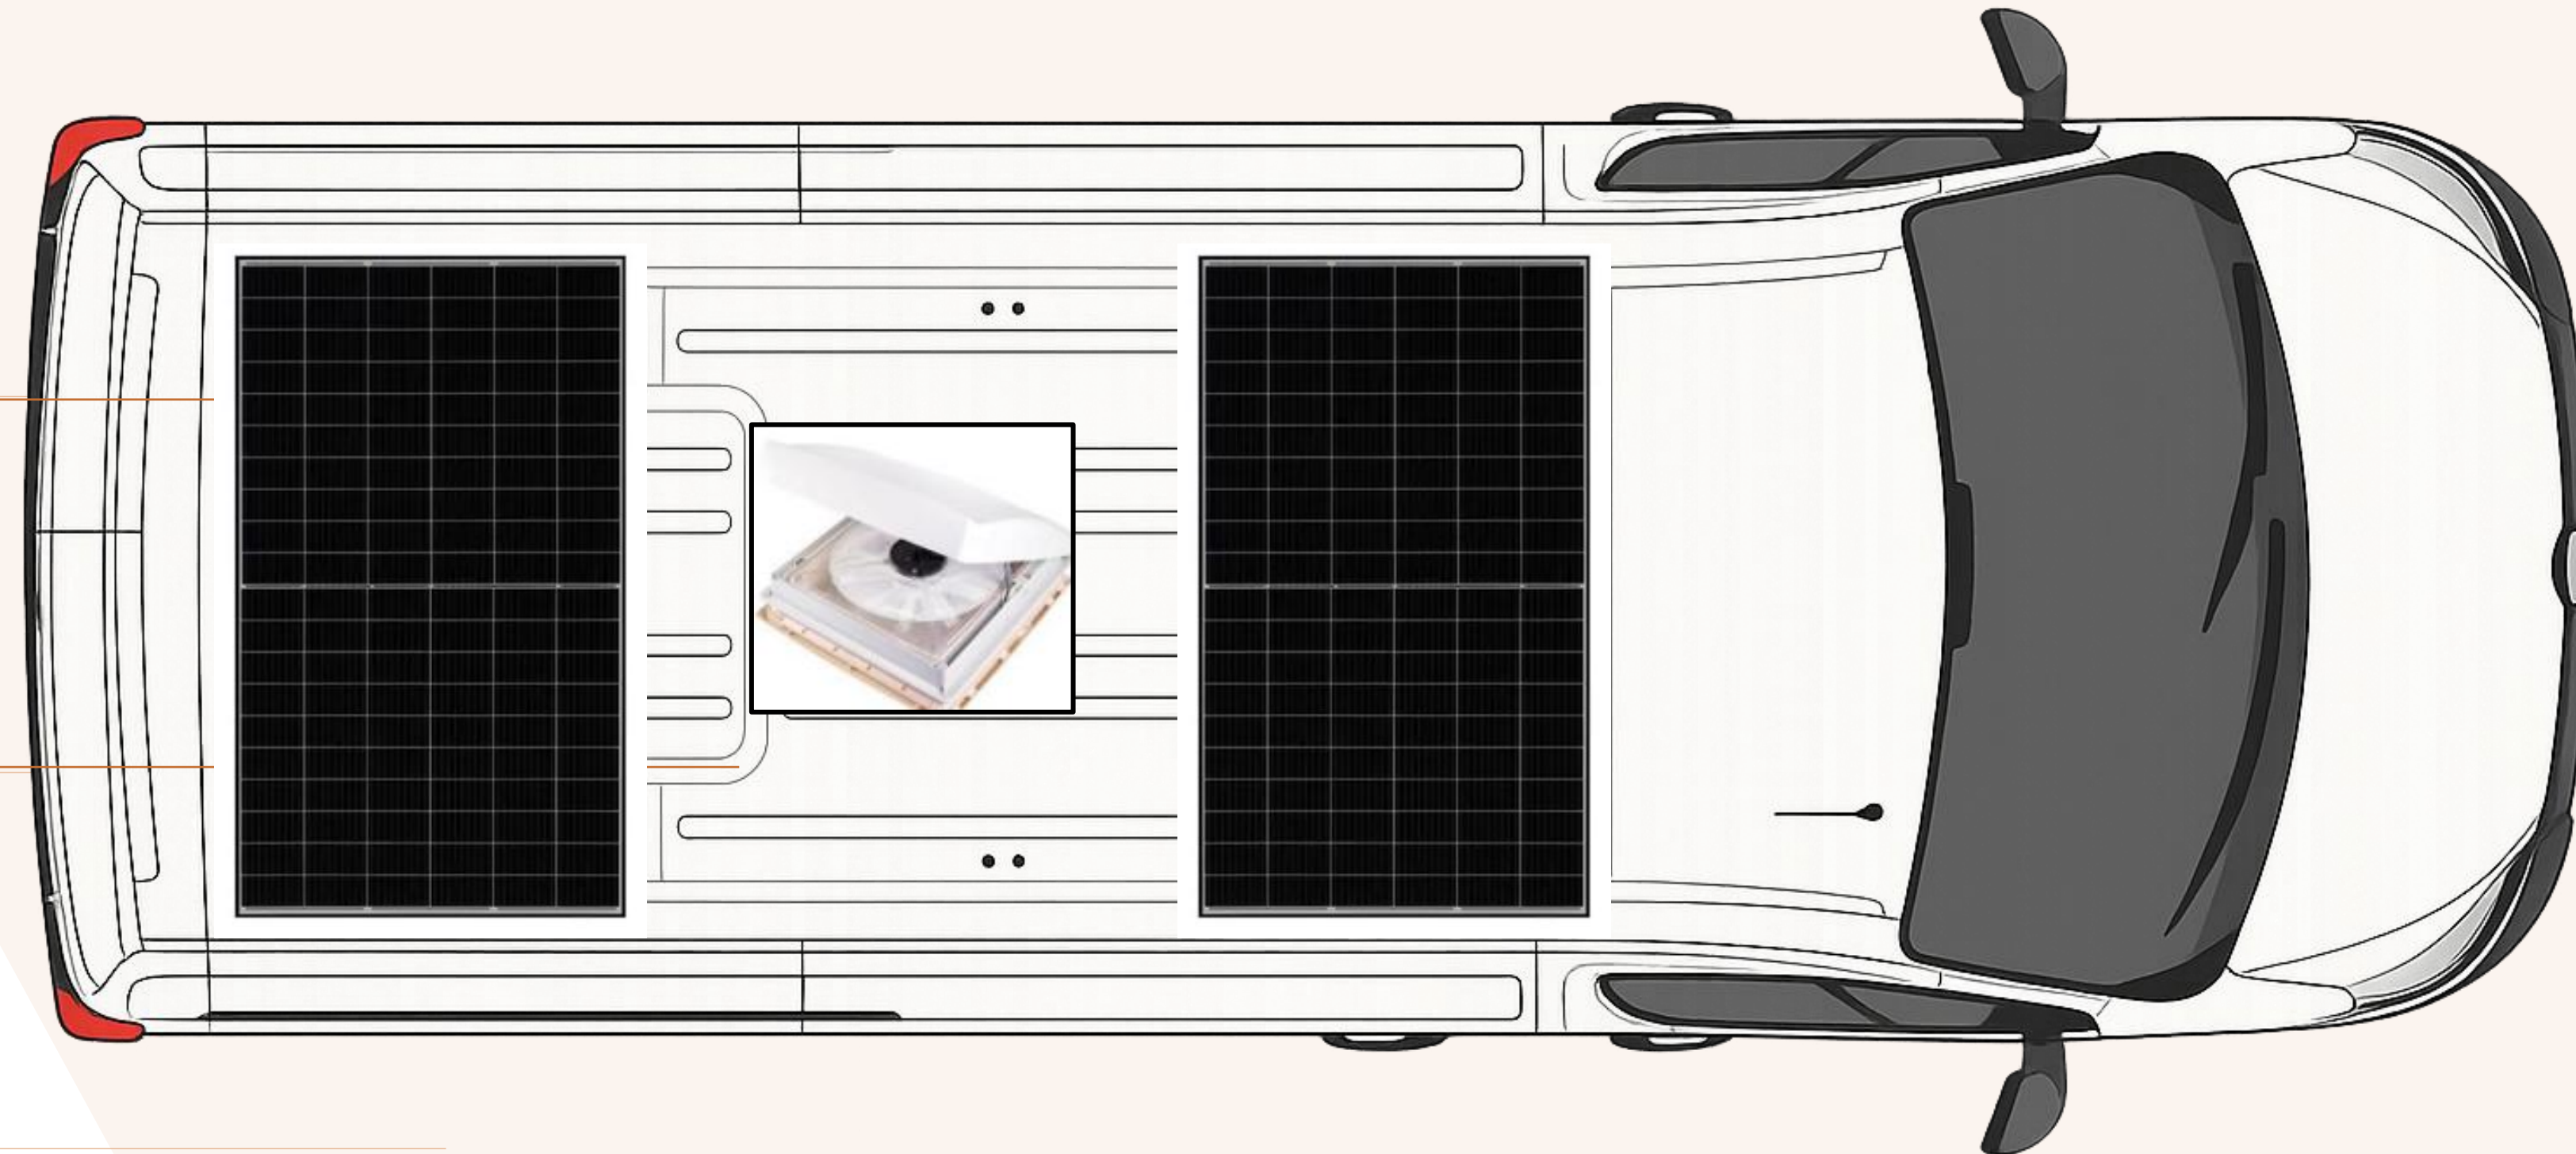

RÉPARTITION DES MEUBLES ET ESPACE DE RANGEMENT


Légende :




Surface de rangement sous le lit




Lit enfant sous Lit adulte

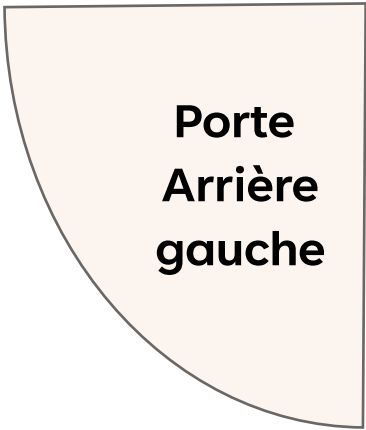

Porte Arrière gauche

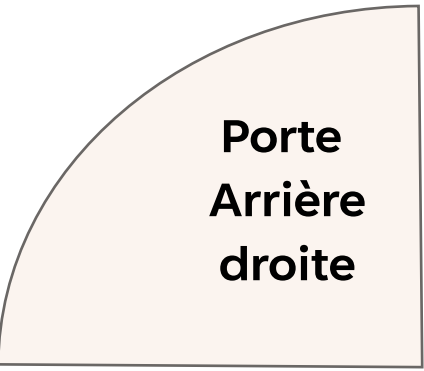

Porte Arrière droite

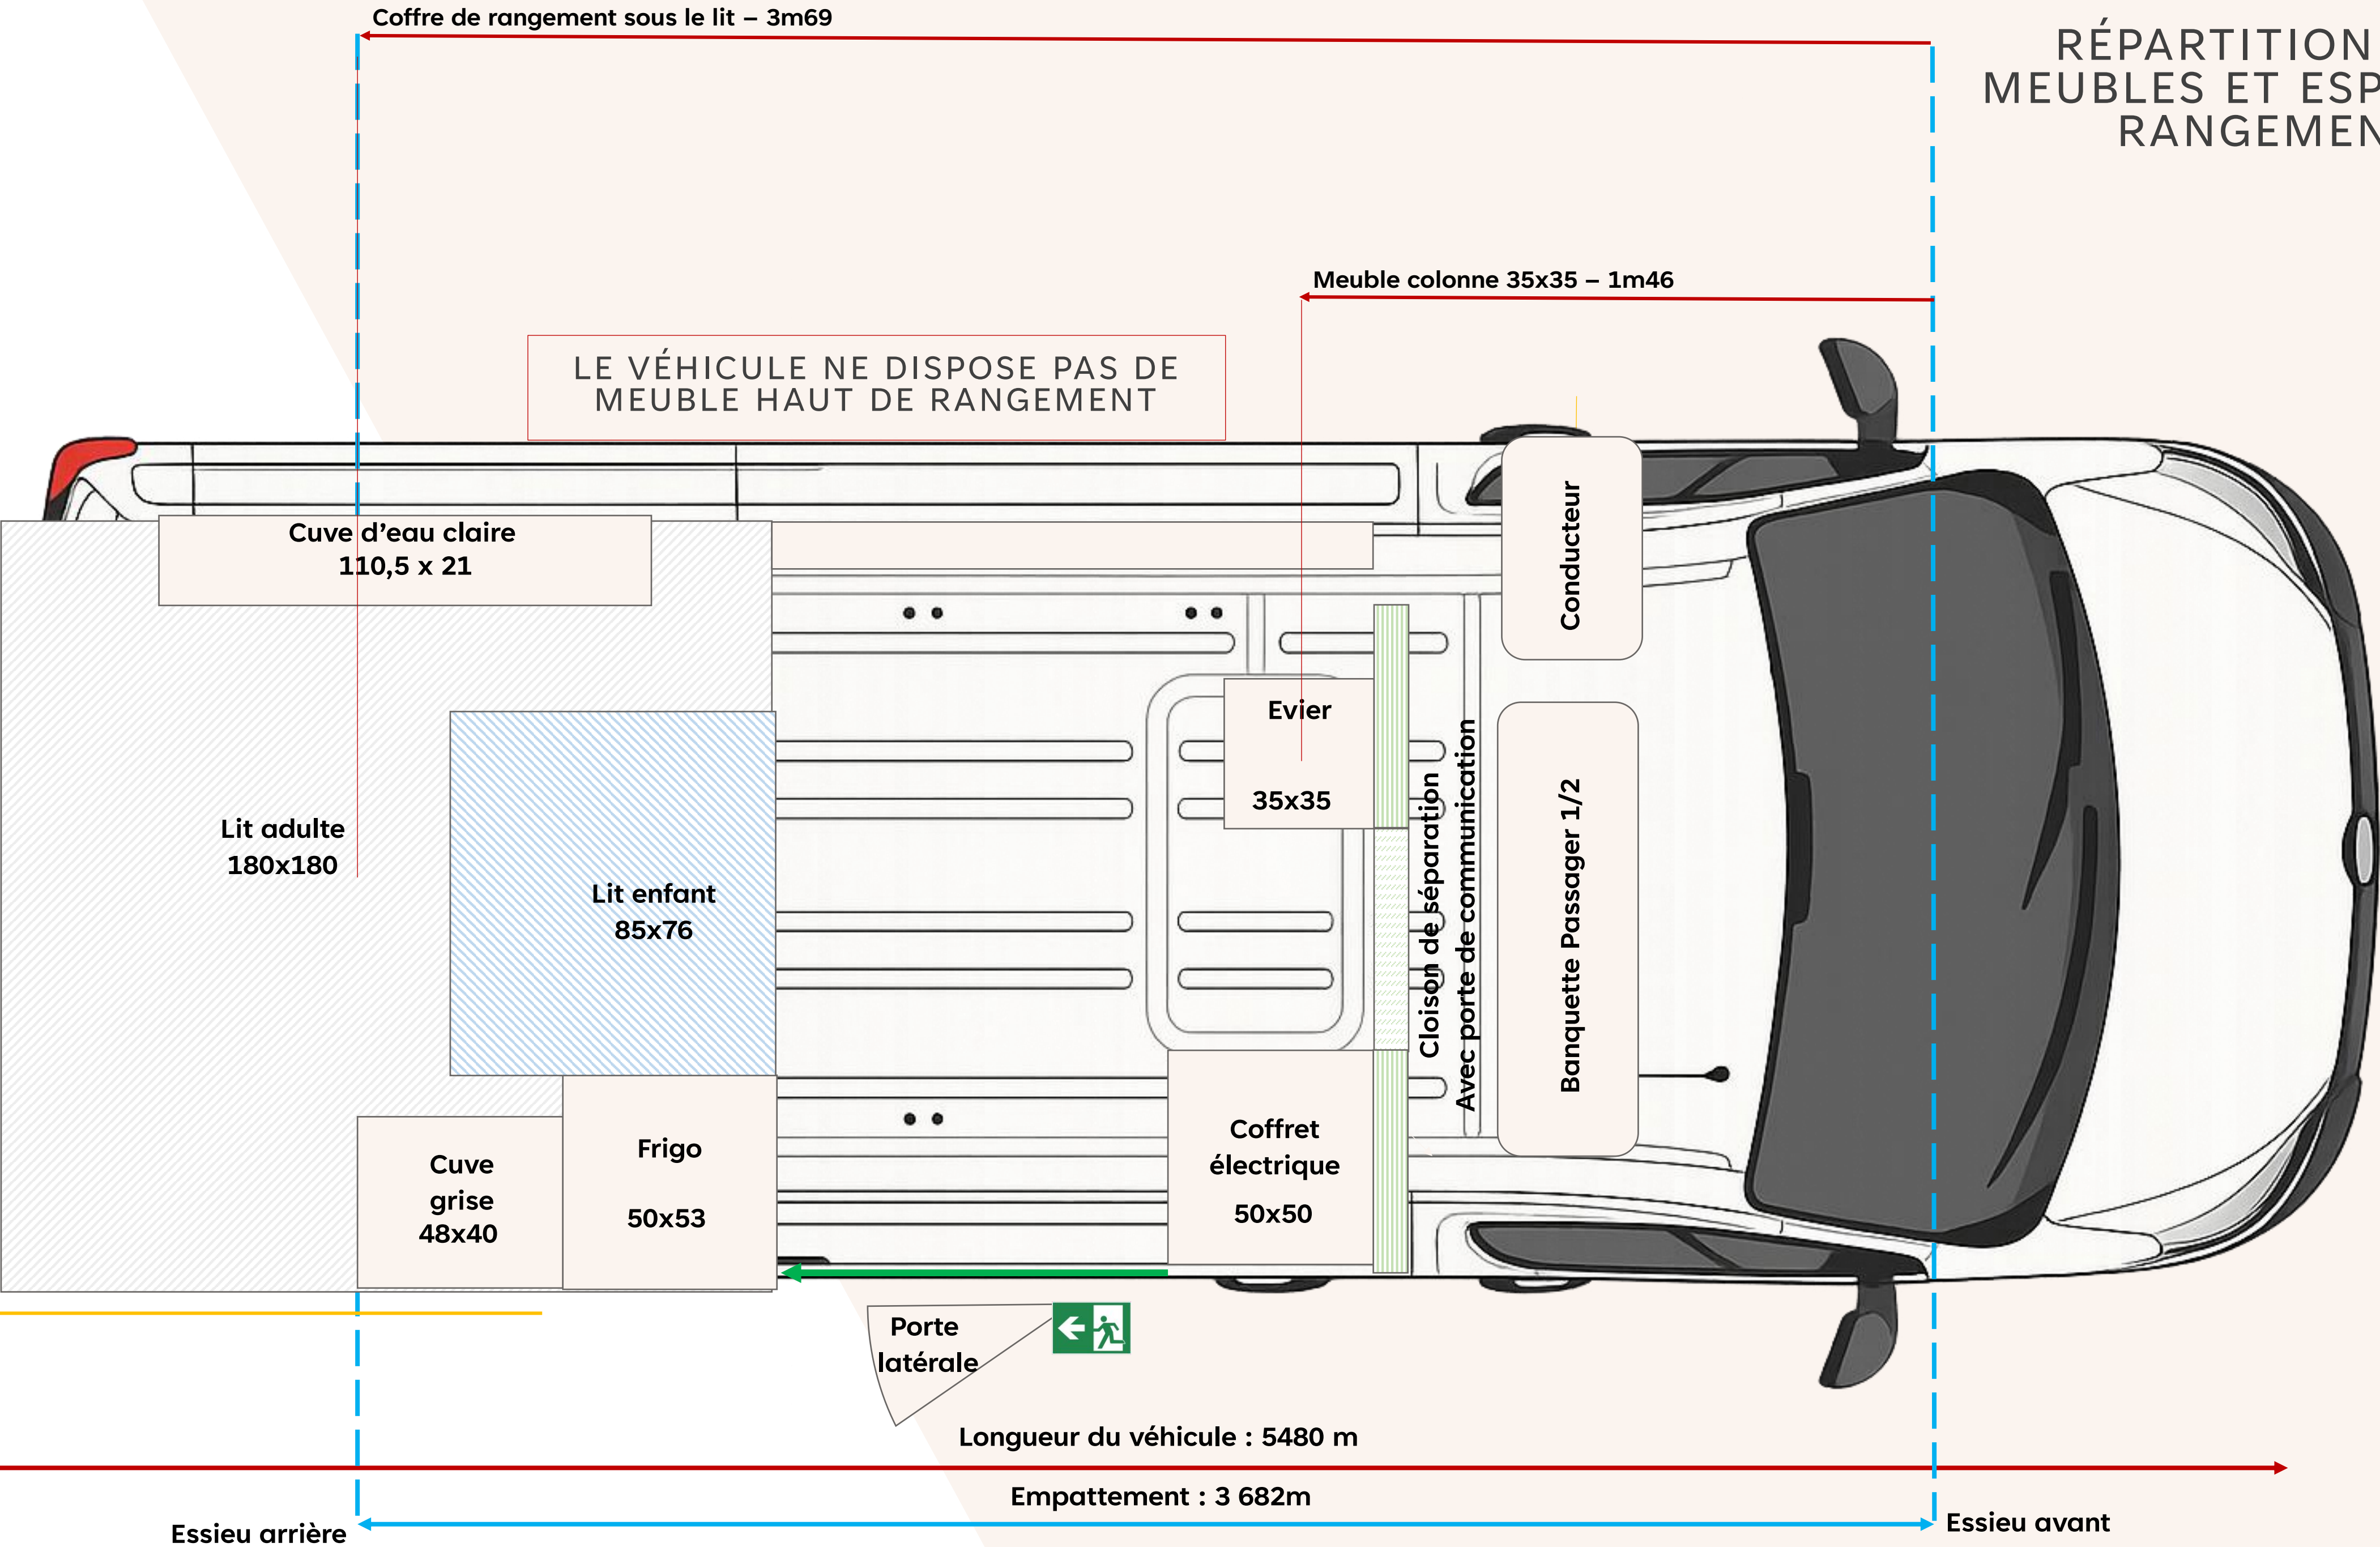

LE VÉHICULE NE DISPOSE PAS DE MEUBLE HAUT DE RANGEMENT

Légende :



Surface de rangement sous le lit



Lit enfant sous Lit adulte

PLAN DE L'ENSEMBLE DES EQUIPEMENTS DU VAN


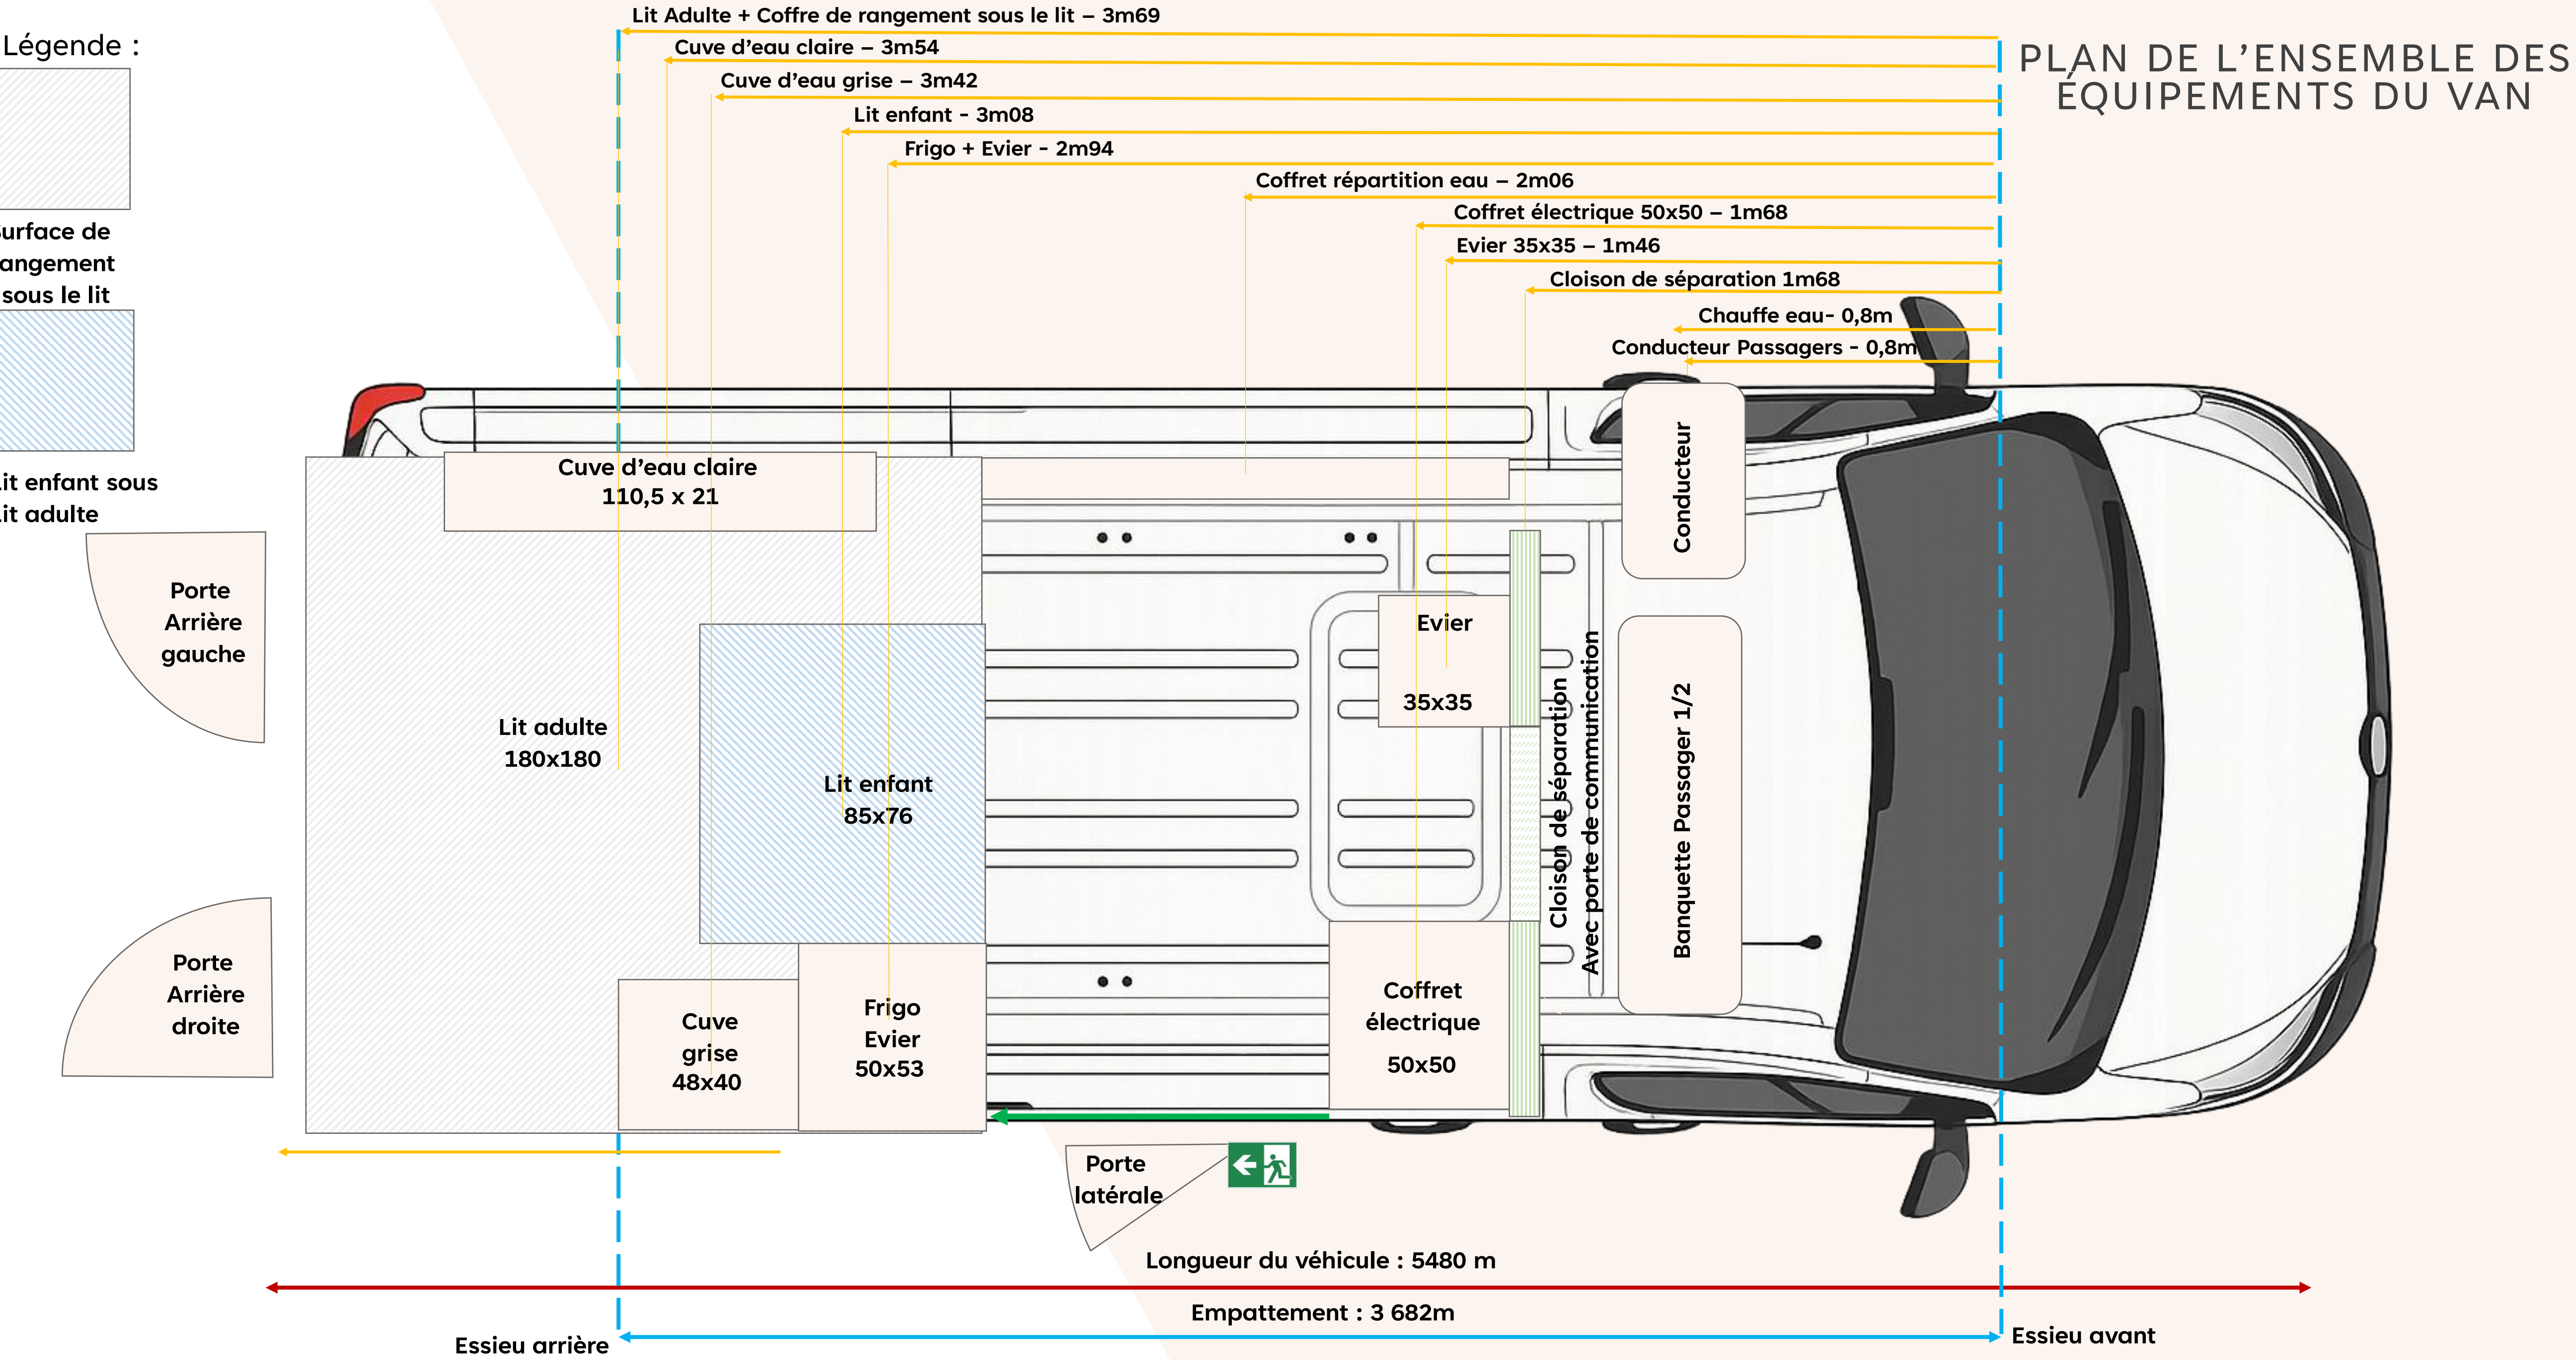


SCHÉMA DU CIRCUIT D'EAU

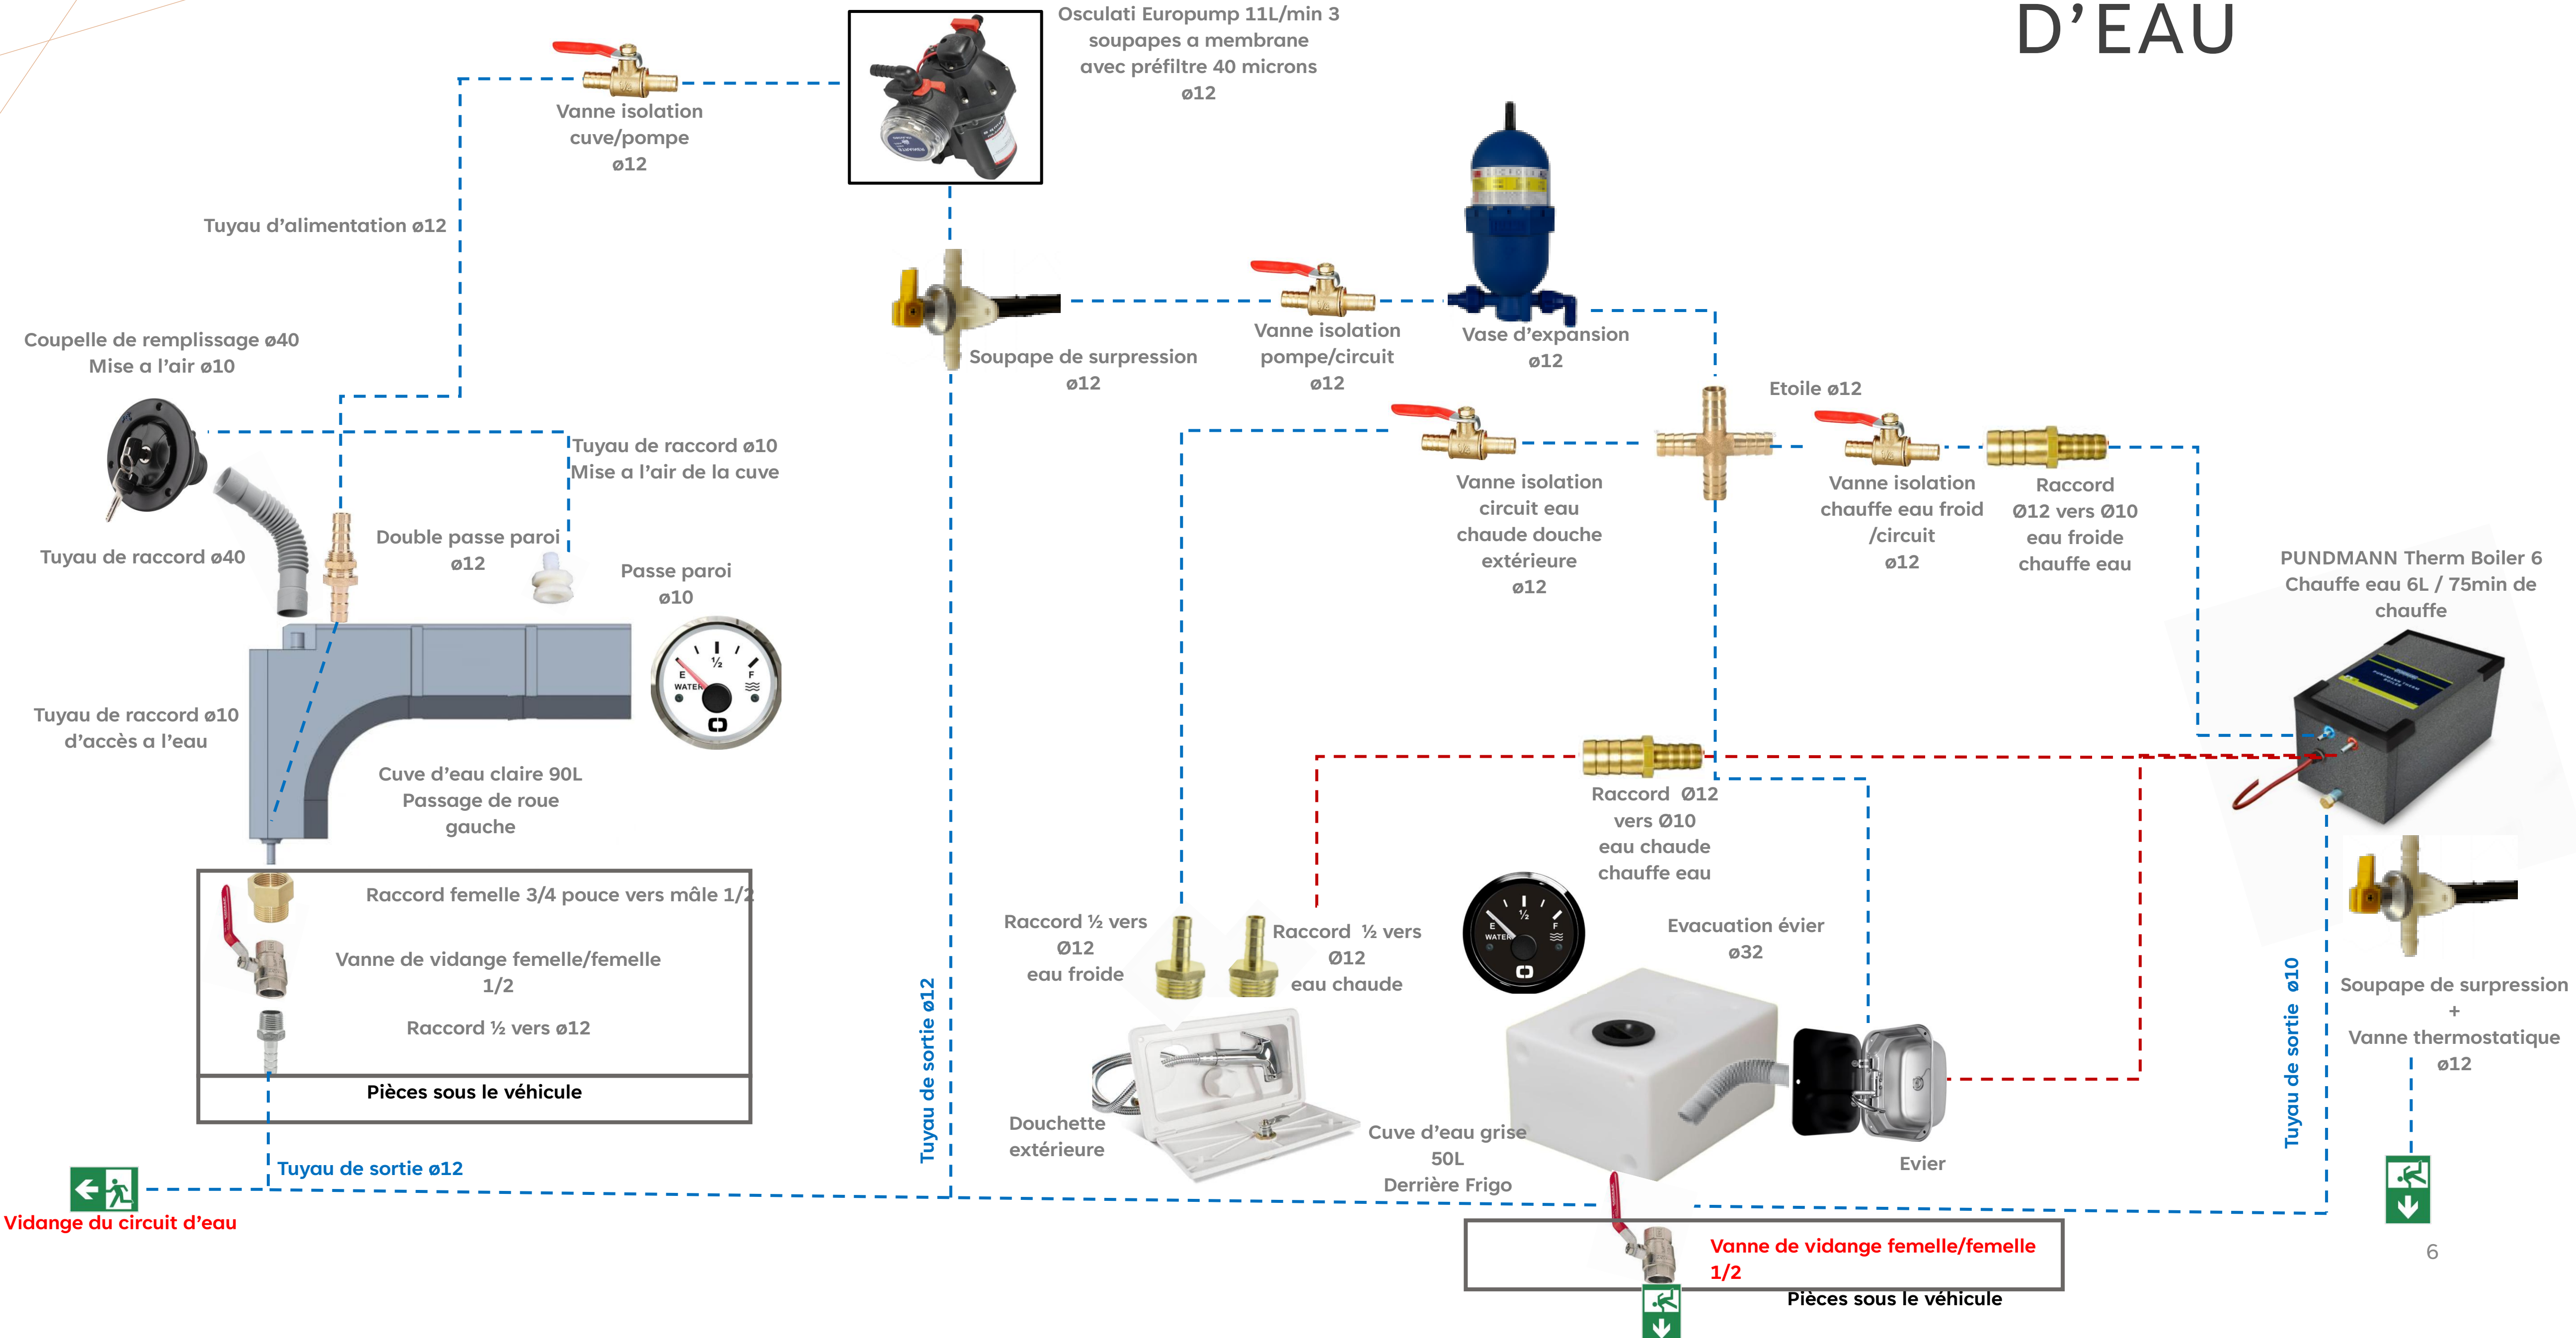

POSITIONNEMENT DES ÉQUIPEMENTS DU CIRCUIT D'EAU

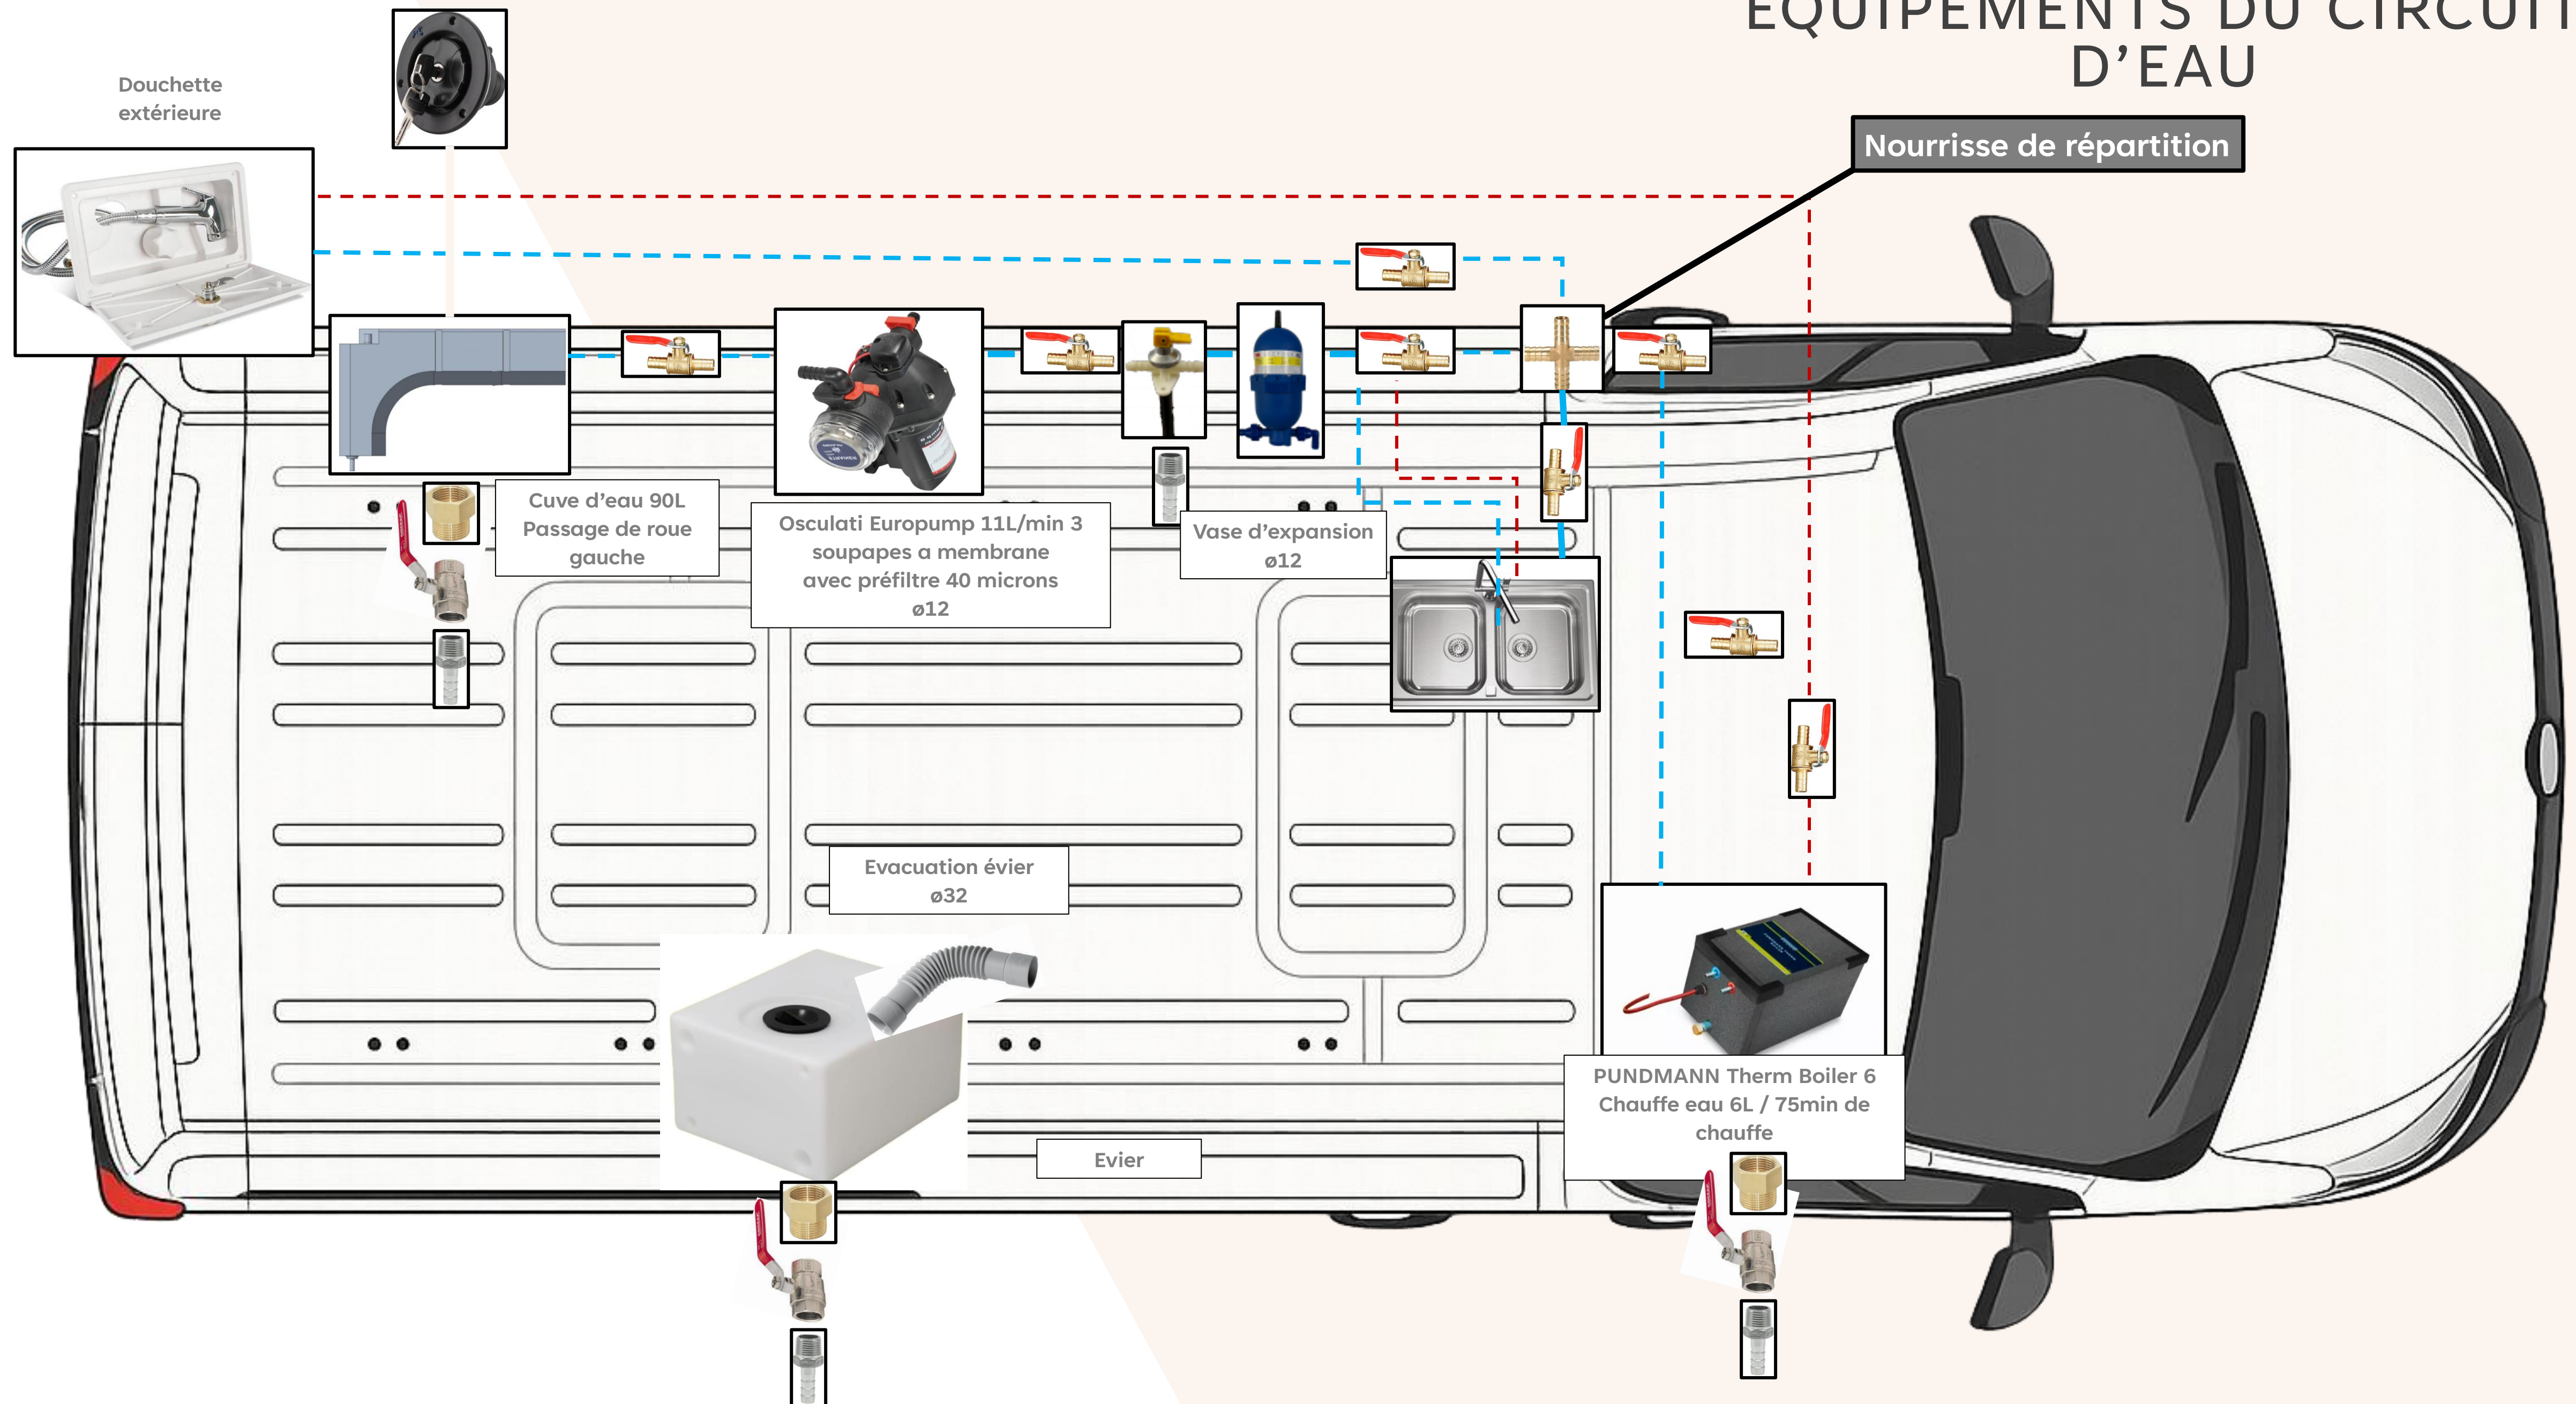


SCHÉMA ÉLECTRIQUE

